



- NOTES:
1. THIS DRAWING IS THE COPYRIGHT OF BLUEHAUS GROUP. IT SHOULD NOT BE RETAINED OR USED WITHOUT WRITTEN CONSENT FROM BLUEHAUS GROUP.
 2. DO NOT SCALE FROM THIS DRAWING.
 3. ALL DIMENSIONS ARE IN MILLIMETERS. LEVELS ARE IN METERS UNLESS NOTED OTHERWISE.
 4. ALL DIMENSIONS ARE TO BE VERIFIED ON SITE AND APPROVED BY THE CONSULTANT/ENGINEER PRIOR TO ANY COMMENCEMENT OF WORK.
 5. THIS DRAWING IS TO BE READ IN CONJUNCTION WITH OTHER RELEVANT ARCHITECTURAL, STRUCTURAL, INTERIOR DESIGN AND MEP DRAWINGS AND ALL RELEVANT SECTIONS OF THE SPECIFICATION DOCUMENTS.
 6. THE CONTRACTOR HAS AN OBLIGATION TO NOTIFY THE CONSULTANT/ENGINEER OF ANY DISCREPANCIES ON THIS DRAWING PRIOR TO COMMENCEMENT OF ANY WORK INCLUDING PRODUCTION OF SHOP DRAWINGS AND / OR PROCUREMENT.

KEY PLAN:

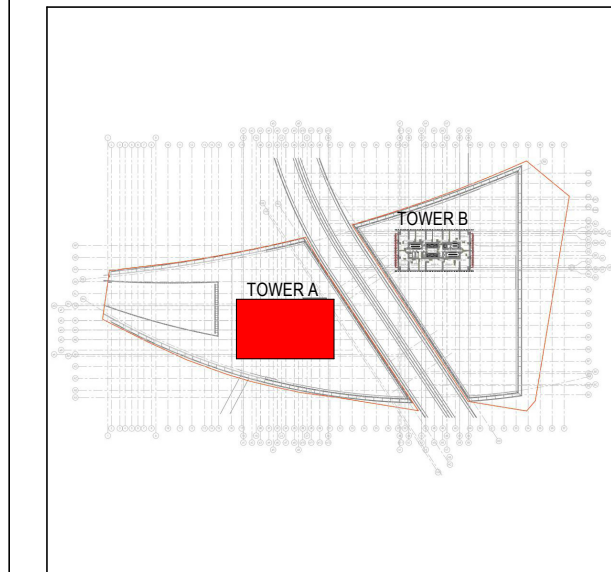

REV. NO.	DATE	DESCRIPTION	REV. BY	CHKD. BY
P01	250425	ISSUED FOR APPROVAL	AJ	MT
P02	250507	REVISION AS CLOUDED	ADG	MT
P03	250613	ISSUED FOR APPROVAL - CD+	ADG	MT
P04	250828	ISSUED FOR APPROVAL - SPATIAL COORDINATION	SKK	SR

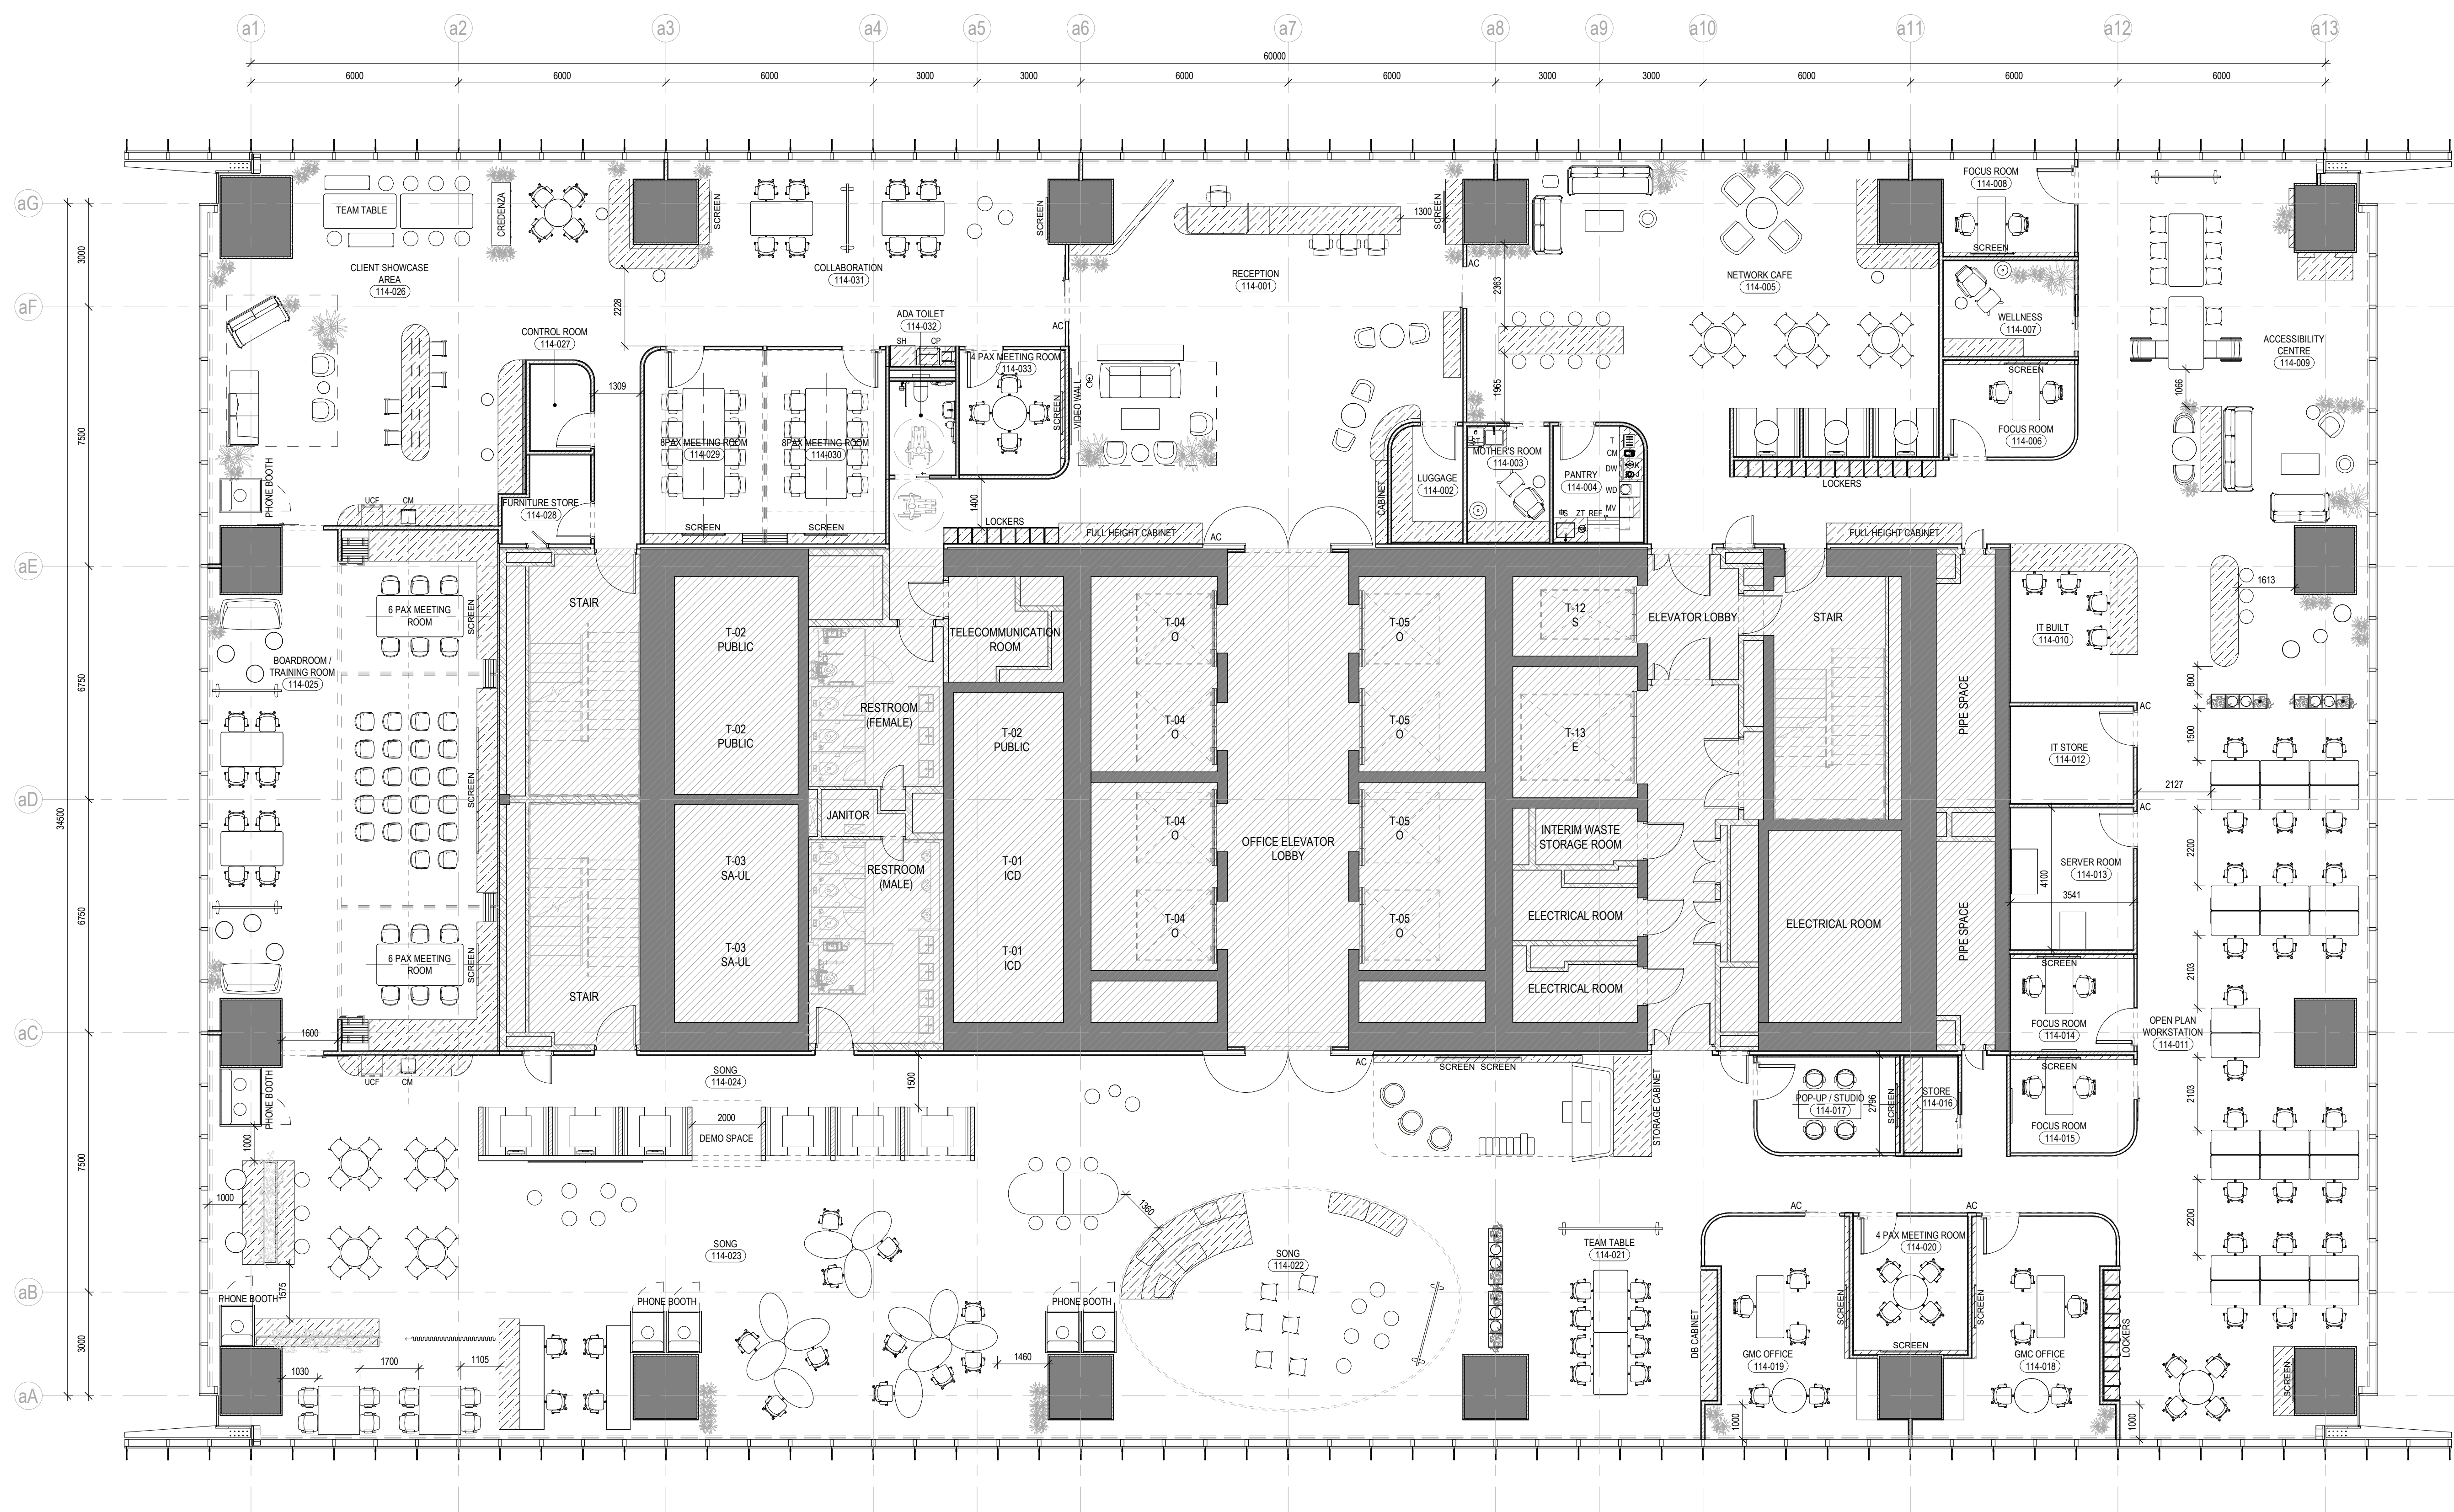

UCF	UNDERCOUNTER FRIDGE
CM	COFFEE MACHINE
K	KETTLE
DW	DISHWASHER

NS	NESPRESSO
J	JUICER
T	TOASTER
ZT	ZIPTAP
SH	SHREDDER
CP	COPY / PRINTER
LED	LED SCREEN
ST	STERILIZER

BASE BUILD LEGEND:	
[Pattern]	OUT OF SCOPE
GENERAL ARRANGEMENT LEGEND:	
[Pattern]	PROPOSED NEW FURNITURE
[Pattern]	CUSTOM MADE JOINERY BY CONTRACTOR
S	SINK
REF	REFRIGERATOR
WD	WATER DISPENSER
MV	MICROWAVE

- NOTES:
- CONTRACTOR AND SUB-CONTRACTORS TO SURVEY EXISTING SITE PRIOR TO COSTING AND MOBILIZATION.
 - FOR CUSTOM MADE ITEMS, PLEASE REFER TO WORKING/DETAIL DRAWINGS.
 - FOR DOOR SCHEDULES, REFER TO 70 SERIES DRAWING.
 - FOR BLOW UP PLAN, REFER TO 40 SERIES DRAWING.
 - FOR ELEVATIONS AND SECTIONS, REFER TO 300 SERIES DRAWING.
 - THIS DRAWING IS TO BE READ IN CONJUNCTION WITH FINISHES NOTED IN PROJECT SPECIFICATIONS. ANY AMBIGUITY IS TO BE BROUGHT TO THE DESIGNERS ATTENTION FOR CLARIFICATION PRIOR TO PRICING AND PROCEEDING WITH THE EXECUTION OF WORKS.

1 LEVEL 14 GENERAL ARRANGEMENT PLAN
SCALE - 1 : 100

CLIENT: **accenture**

LEAD CONSULTANT/ DESIGN ARCHITECT:

BLUEHAUS
a tp bennett company

CONTACT: www.bluehausgroup.com/contact

PROJECT: **ACCENTURE_OZ**

PROJECT LOCATION: **ONE ZA'ABEEL TOWER**

DRAWING TITLE: **GENERAL ARRANGEMENT PLAN - LEVEL 14 OPTION-01**

DRAWN BY:	SHL	CHECK BY:	ML	APP. BY:	DC	DESIGN STAGE:
SCALE:	1 : 100	SHEET SIZE:	A1	CURRENT REV. DATE:	250828	SC
DRAWING NO.:	BH3198-BHG-OFF-14-DRG-ID-21140	REVISION:				P04

Intellectual Property of Bluehaus Group